
Gebruikte bronnen:
Constructie: IMd: 27-07-2018

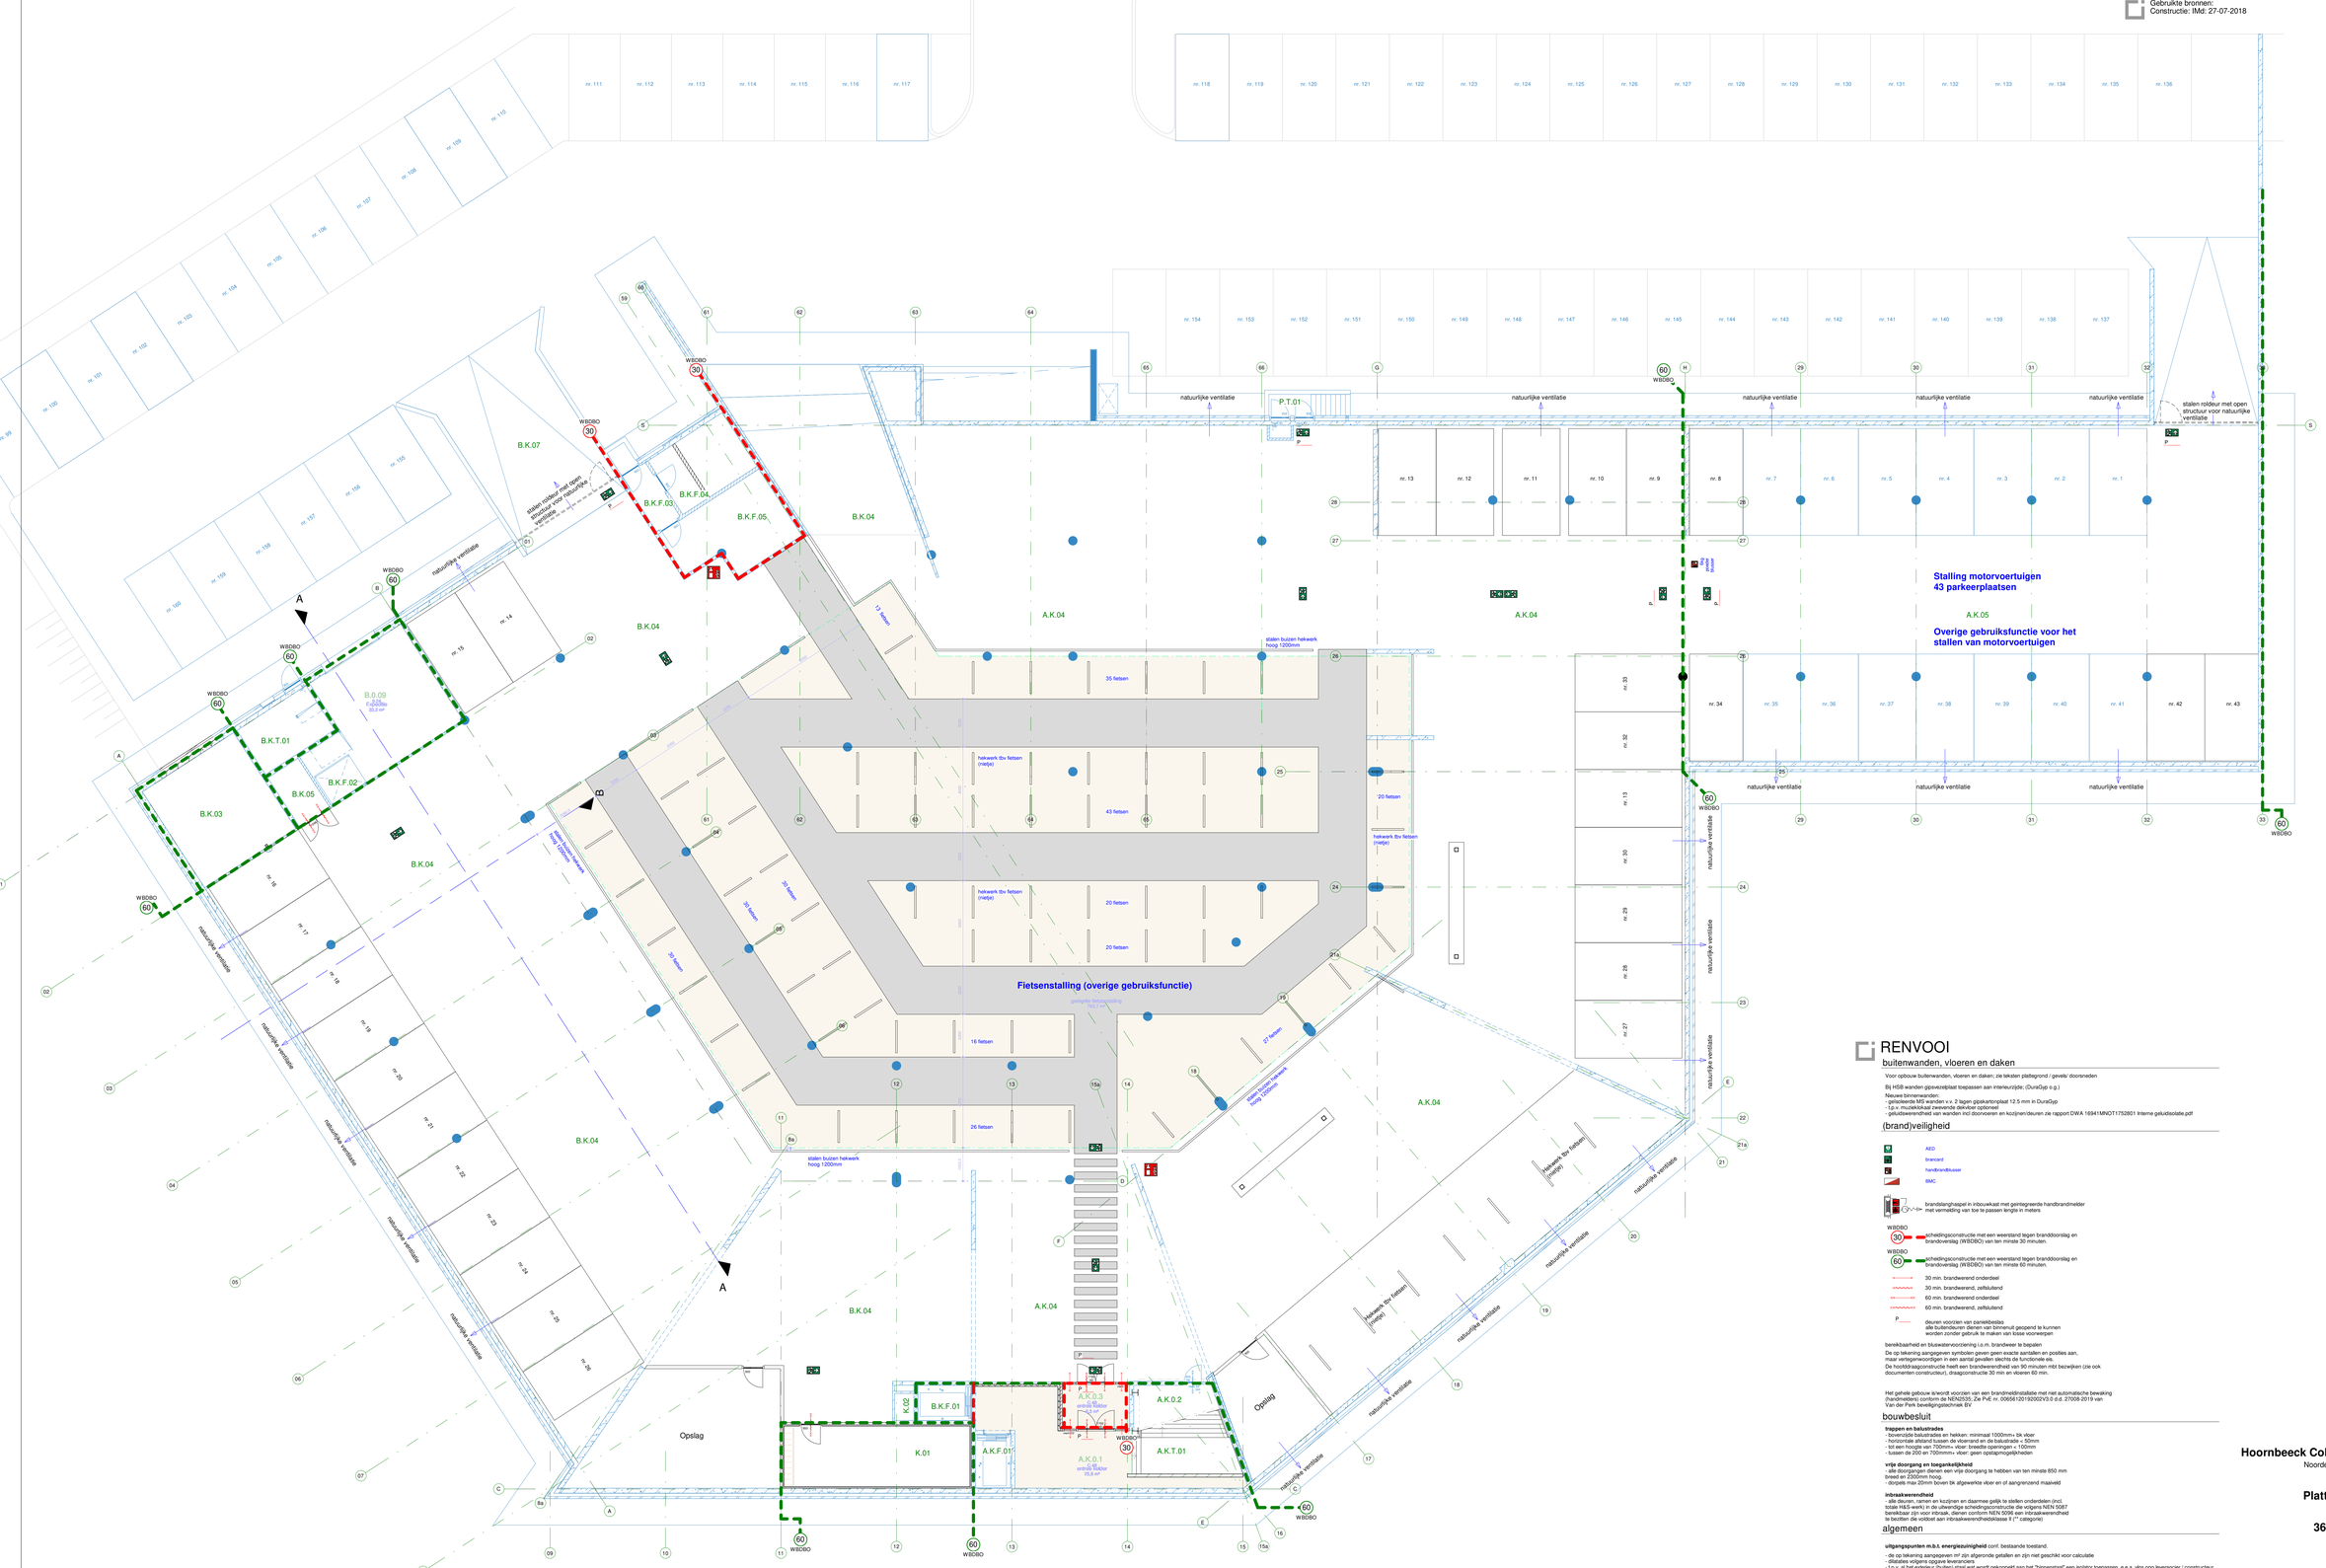

RENVOOI

buitenwanden, vloeren en daken

Voor opbouw buitenwanden, vloeren en daken; zie teksten plattegrond / gevels/ doorsneden

Bij HSB wanden gipsvezelplaat toepassen aan interieurzijde. (DuraGyp o.g.)

Nieuwe binnenwanden:
- gelaste MS wanden v.v. 2 lagen gipskartonplaat 12,5 mm in DuraGyp
- t.p.v. muziekloksaal zeewende delvibar optioneel
- geluidswerendheid van wanden incl doorvoeren en kozijnen/deuren zie rapport DWA 16941MNOT1752801 Interne geluidsisolatie.pdf

(brand)veiligheid

- AED
- brancard
- handbrandblusser
- BMC
- brandslanghaspel in inbouwkast met geintegreerde handbrandmelder
- met vermelding van toe te passen lengte in meters
- WBDBO 30 — scheidingsconstructie met een weerstand tegen branddoorslag en brandoverslag (WBDBO) van ten minste 30 minuten.
- WBDBO 60 — scheidingsconstructie met een weerstand tegen branddoorslag en brandoverslag (WBDBO) van ten minste 60 minuten.
- 30 min. brandwerend onderdeel
- 30 min. brandwerend, zelfsluitend
- 60 min. brandwerend onderdeel
- 60 min. brandwerend, zelfsluitend
- deuren voorzien van paniekbeslag
 alle buitendeuren dienen van binnenuit geopend te kunnen worden zonder gebruik te maken van losse voorwerpen

bereikbaarheid en bluswatervoorziening i.o.m. brandweer te bepalen

De op tekening aangegeven symbolen geven geen exacte aantallen en posities aan, maar vertegenwoordigen in een aantal gevallen slechts de functionele eis.

De hoofddraagconstructie heeft een brandwerendheid van 90 minuten mbt bezwijken (zie ook documenten constructeur), draagconstructie 30 min en vloeren 60 min.

Het gehele gebouw is/wordt voorzien van een brandmeldinstallatie met niet automatische bewaking (handmelders) conform de NEN2535; Zie PvE nr. 0065612019200ZV3.0 d.d. 27008-2019 van Van der Perk beveiligingsadviesbureau BV

bouwbesluit

trappen en balustrades
- Aaneengesloten balustrades en hekken: minimaal 1000mm+ bk vloer
- horizontale afstand tussen de vloerrand en de balustrade < 50mm
- tot een hoogte van 700mm+ vloer: breedte openingen < 100mm
- tussen de 200 en 700mm+ vloer: geen opstapmogelijkheden

vrije doorgang en toegankelijkheid
- alle doorgangen dienen een vrije doorgang te hebben van ten minste 850 mm breed en 2300mm hoog.
- dorpels max 20mm boven bk afgewerkte vloer en of aangrenzend maaiveld

inbraakwerendheid
- alle deuren, ramen en kozijnen en daarmee gelijk te stellen onderdelen (incl. totale H&S-werk) in de uitwendige scheidingsconstructie die volgens NEN 5087 bereikbaar zijn voor inbraak, dienen conform NEN 5096 een inbraakwerendheid te bezitten die voldoet aan inbraakweerendheidsklasse II (** categorie)

algemeen

uitgangspunten m.b.t. energieuitvingheid conf. bestaande toestand.

- de op tekening aangegeven m² zijn afgerondde getallen en zijn niet geschikt voor calculatie
- dilataties volgens opgave leveranciers
- t.p.v. al het exterieur (buiten) staat wat wordt gekoppeld aan het "binnenstaat" een isolator toepassen, e.e.a. vlgs opg leverancier / constructeur
- overig hulpstaal vlgs opg leverancier / constructeur

verwijzingen

- voor constructieve gegevens:	zie tek. / berekeningen IMd	
- geotechnisch onderzoek	zie memo:	208741-10_M01
- voor brandveiligheid		
- voor geluidwering (intern):	zie rapport	16941MNOT1752801 Interne geluidsisolatie
- voor geluidwering (extern):	zie rapport	2017-12-18 M2017090500P002
- voor ventilatie	zie rapport	

F 01-09-2020: gewijzigd
01-08-2019: datum

Hoornbeeck College te Gouda: project
Noordelijk halfrond 10, Gouda: adresgegevens
Hoornbeeck College: opdrachtgever

Plattegrond kelder: onderdeel
1 : 100: schaal

3690-DO-090-AO: project- en tekeningnummer
Omgevingsvergunning: projectfase

J. Orgers: projectmanager
J. Hofland: getekend

RoosRos Architecten
L.J. Costerstraat 2 | 3261 LH
Postbus 1631 | 3260 BC
Oud-Beijerland

0186 69 15 80
info@roosros.nl
www.roosros.nl

ROOSROS ARCHITECTEN