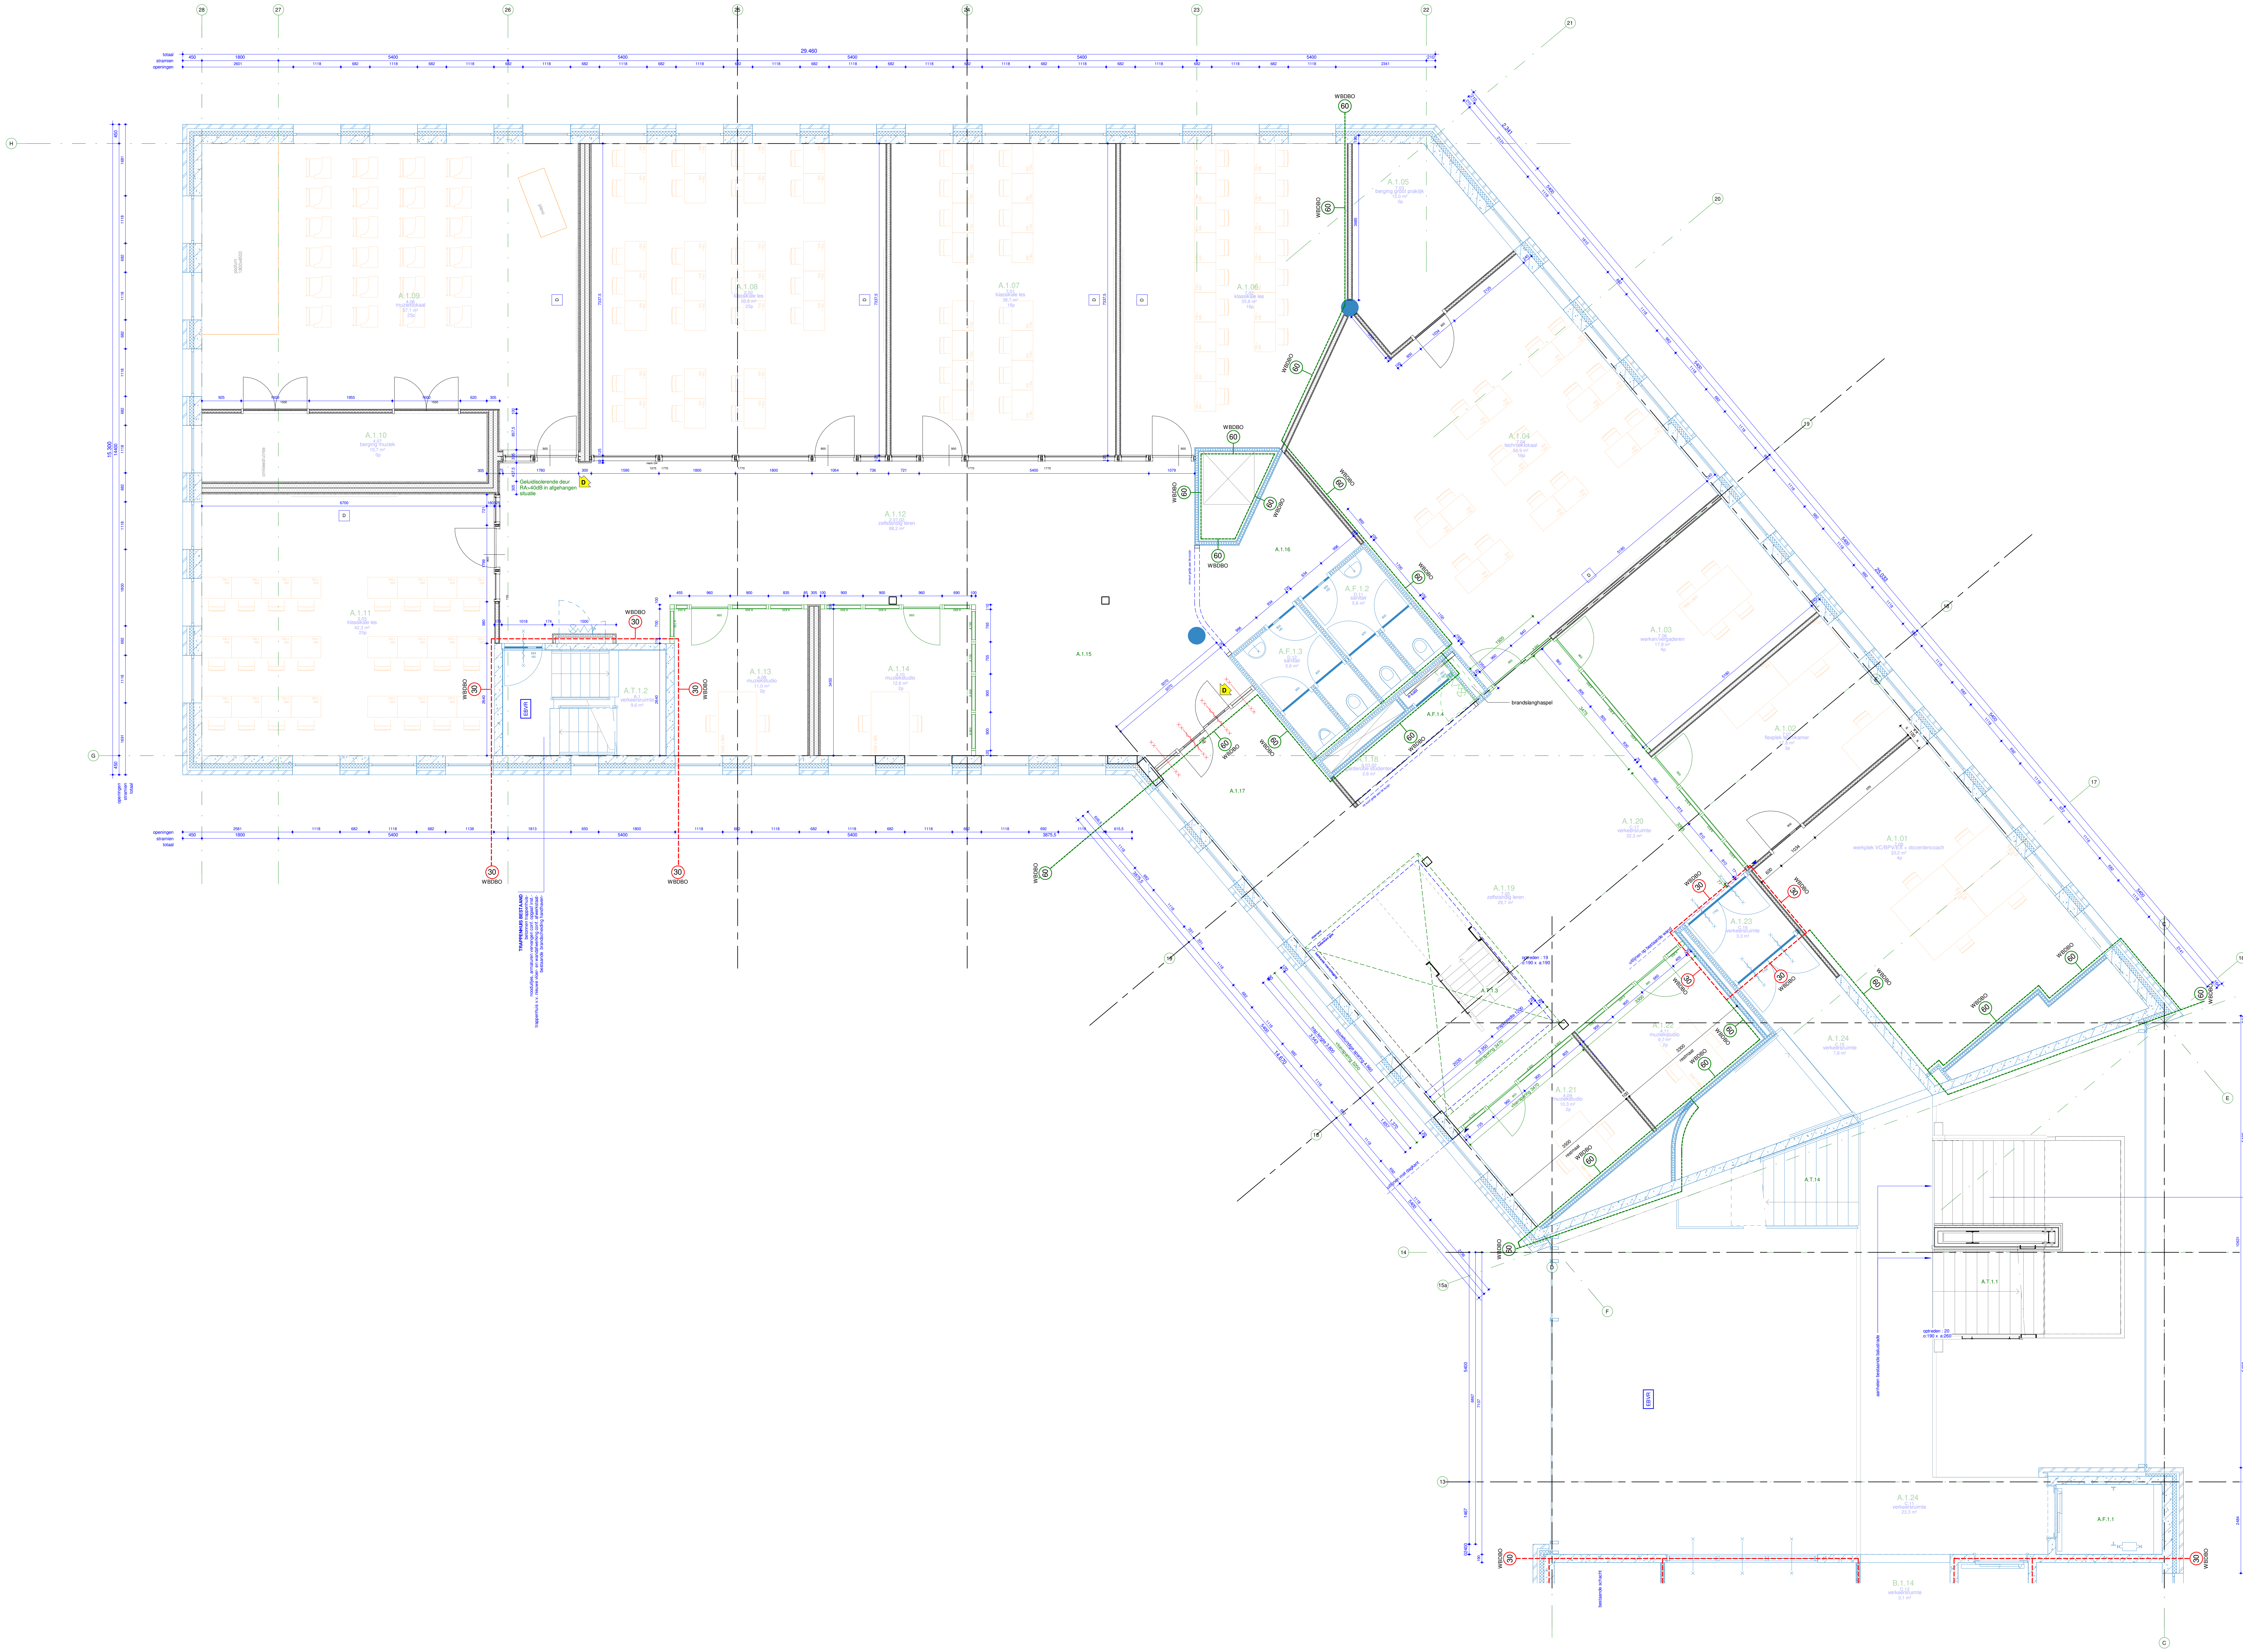

eerste verdieping A
1 : 50

RENVOOI

De aanvraag betreft een transformatie van een kantoorgebouw naar een schoolgebouw. De vergunning voor de bestemmingsplanwijziging is reeds verleend. Deze aanvraag omgevingsvergunning betreft alleen de onderdelen m.b.t. de constructieve en brandscheidingen/ compartimentering. De onderdelen waar we vergunning voor aanvragen zijn in kleur aangegeven, de overige delen zijn grijs weergegeven.

buitenwanden, vloeren en daken

Voor opbouw buitenwanden, vloeren en daken; zie teksten plattegrond / gevels/ doorsneden

Bij HSB wanden gipsvezelplaat toepassen aan interieurzijde; (DuraGyp o.g.)

Nieuwe binnenwanden:
- geïsoleerde MS wanden v.v. 2 lagen gipskartonplaat 12.5 mm in DuraGyp
- t.p.v. muzieklokaal zwevende dekvloer optioneel
- geluidswerendheid van wanden incl doorvoeren en kozijnen/deuren zie rapport DWA 16941MNOT1752801 Interne geluidisolatie.pdf

fasering

▨	bestaande elementen	☐	interieur onderdelen (buiten opdracht)
▨	onderdelen vergunning	▨	bestaand/vergunningsvrij

brandveiligheid

vluchtroute-aanduiding, noodverlichting en installatieonderdelen conform rapport DWA 16941MNOT1695946 Brandveiligheid 3

brandslanghaspel in inbouwkast met geintegreerde handbrandmelder met vermelding van toe te passen lengte in meters

WBDBO 30 – scheidingsconstructie met een weerstand tegen branddoorslag en brandoverslag (WBDBO) van ten minste 30 minuten.

WBDBO 60 – scheidingsconstructie met een weerstand tegen branddoorslag en brandoverslag (WBDBO) van ten minste 60 minuten.

WBDBO 60 – weerstand tegen brandoverslag bovendaks: 60 minuten (gecertificeerde oplossing i.o.m. brandweer)

- 30 min. brandwerend onderdeel
- 30 min. brandwerend, zelfsluitend
- 60 min. brandwerend onderdeel
- 60 min. brandwerend, zelfsluitend

P – deuren voorzien van paniekbeslag
alle buitendeuren dienen van binnenuit geopend te kunnen worden zonder gebruik te maken van losse voorwerpen

bereikbaarheid en bluswatervoorziening i.o.m. brandweer te bepalen

De op tekening aangegeven symbolen geven geen exacte aantallen en posities aan, maar vertegenwoordigen in een aantal gevallen slechts de functionele eis.

De hoofddraagconstructie heeft een brandwerendheid van 90 minuten mbt bezwijken (zie ook documenten constructeur), draagconstructie 30 min en vloeren 60 min.

bouwbesluit

trappen en balustrades
- bovenzijde balustrades en hekken: minimaal 1000mm+ bk vloer
- horizontale afstand tussen de vloerrand en de balustrade < 50mm
- tot een hoogte van 700mm+ vloer: breedte openingen < 100mm
- tussen de 200 en 700mmm+ vloer: geen opstapmogelijkheden

vrije doorgang en toegankelijkheid
- alle doorgangen dienen een vrije doorgang te hebben van ten minste 850 mm breed en 2300mm hoog.
- dorpels max 20mm boven bk afgewerkte vloer en of aangrenzend maaiveld

inbraakwerendheid
- alle deuren, ramen en kozijnen en daarmee gelijk te stellen onderdelen (incl. totale H&S-werk) in de uitwendige scheidingsconstructie die volgens NEN 5087 bereikbaar zijn voor inbraak, dienen conform NEN 5096 een inbraakwerendheid te bezitten die voldoet aan inbraakwerendheidsklasse II (** categorie)

uitgangspunten m.b.t. energiezuinigheid conf. bestaande toestand.

algemeen

- de op tekening aangegeven m² zijn afgeronde getallen en zijn niet geschikt voor calculatie
- dilataties volgens opgave leveranciers
- t.p.v. al het exterieur (buiten) staal wat wordt gekoppeld aan het "binnenstaal" een isolator toepassen, e.e.a. vlgs opg leverancier / constructeur
- overig hulpstaal vlgs opg leverancier / constructeur

verwijzingen

- voor constructieve gegevens:	zie tek. / berekeningen IMd	
- geotechnisch onderzoek	zie memo	208741-10_M01
- voor brandveiligheid:	zie rapport	16941MNOT1695946 Brandveiligheid3
- voor geluidwering (intern):	zie rapport	16941MNOT1752801 Interne geluidisolatie
- voor geluidwering (extern):	zie rapport	2017-12-18 M2017090500P002
- voor ventilatie	zie rapport	

geluidswering

conclusie geluidswerende maatregelen gevel:
(zie rapport 2017-12-18 M2017090500P002)

■	pui entreehal, geen ingrepen
🟥	glas vervangen door explosieveilig glas + kierdichting vervangen door dubbele kierdichting
🟧	kierdichting vervangen door dubbele kierdichting
🟩	bestaande kier- en naaddichting vervangen + nalopen knevelende werking en zo nodig vervangen
🟩	bestaande kierdichting nalopen op lekken en zo nodig vervangen
☐	bestaande kierdichting nalopen op lekken en zo nodig vervangen

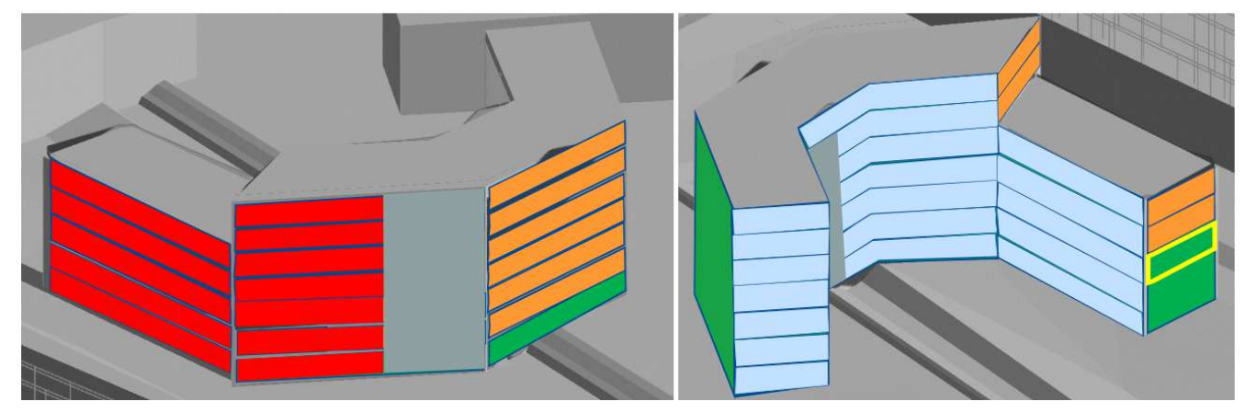

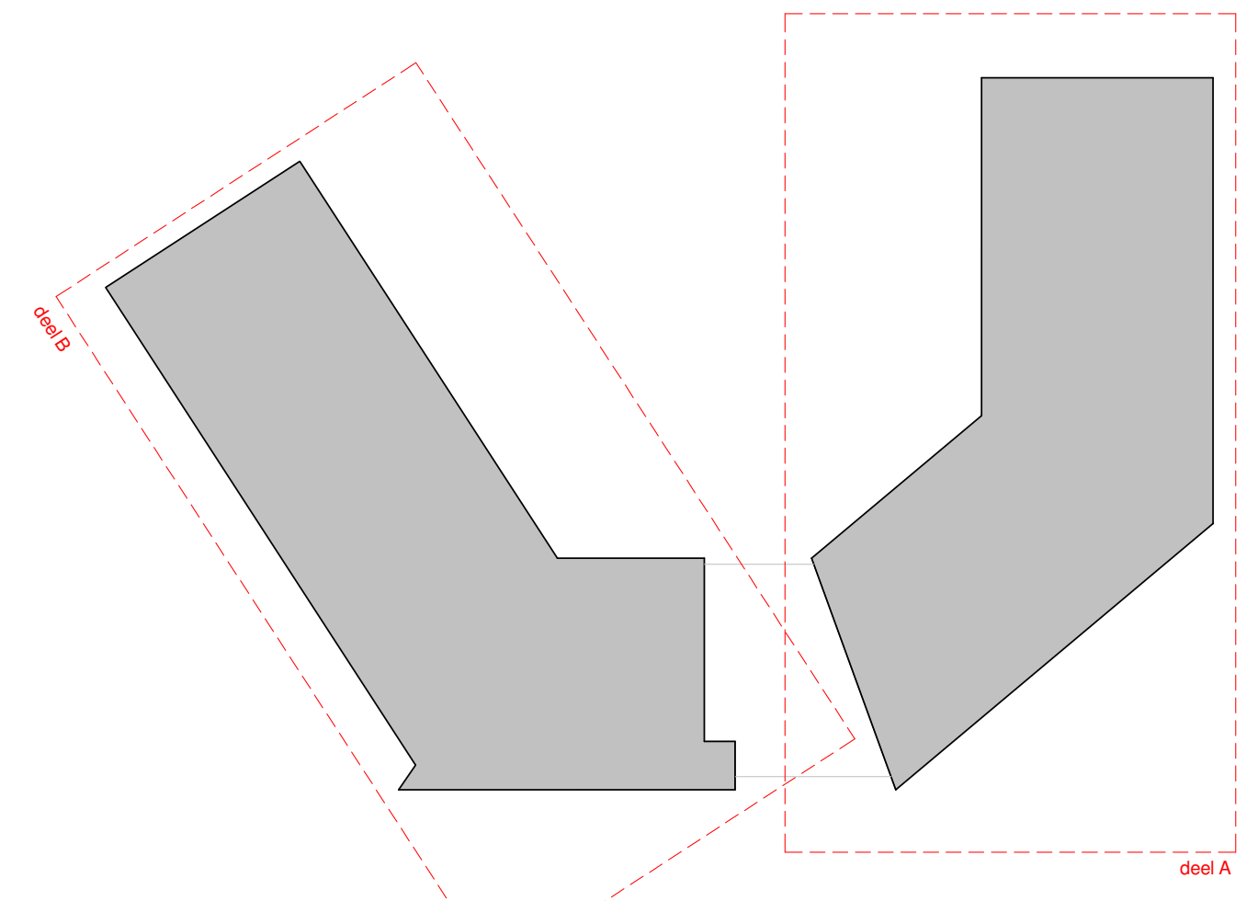

D: 12.02.2019: gewijzigd
14.12.2018: datum

Hoornbeeck College te Gouda: project
Noordelijk halfrond 10, Gouda: adresgegevens
Hoornbeeck College: opdrachtgever

Uitvoeringsgereed: onderdeel
As indicated: schaal

3690-UG-110-A: project- en tekeningnummer
Uitvoeringsgereed: projectfase

Approver: projectmanager
Author: getekend

RoosRos Architecten
L.J. Costerstraat 2 | 3261 LH
Postbus 1631 | 3260 BC
Oud-Beijerland

0186 69 15 80
info@roosros.nl
www.roosros.nl

DEFINITIEF

ROOSROS
ARCHITECTEN